


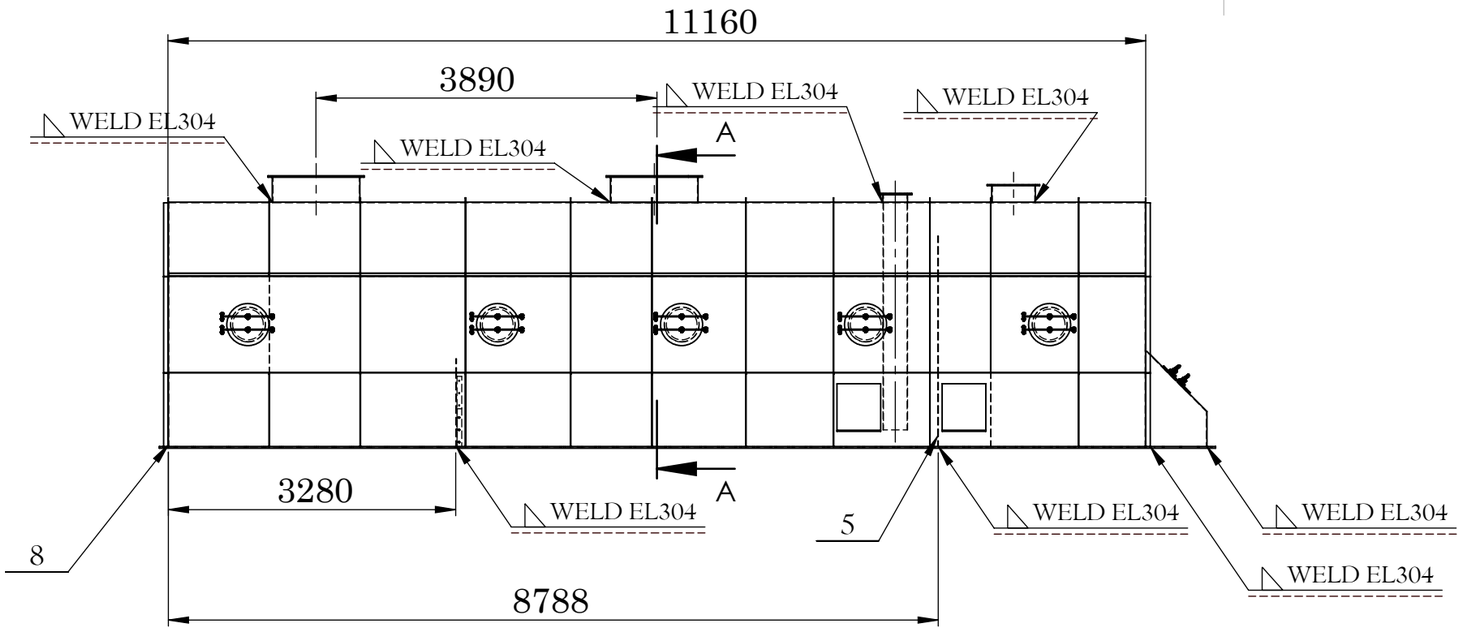


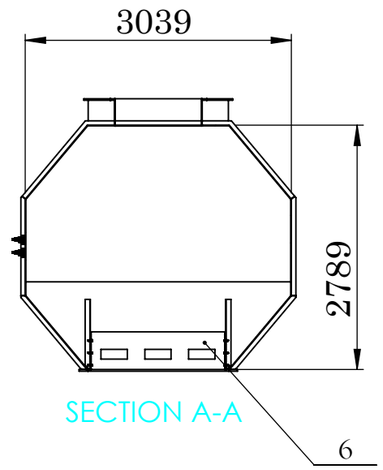

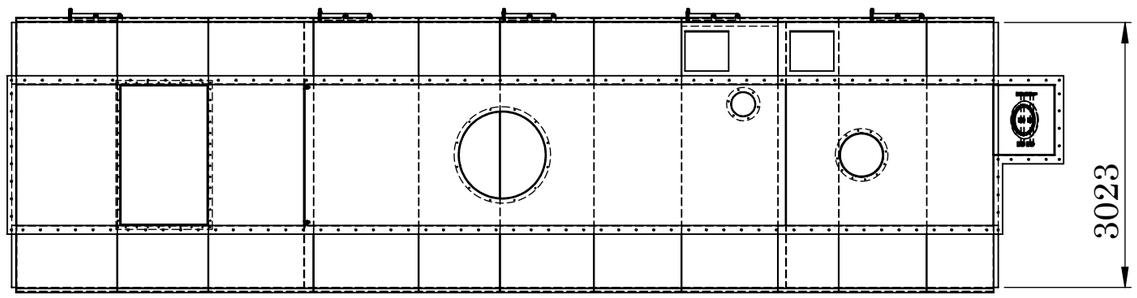

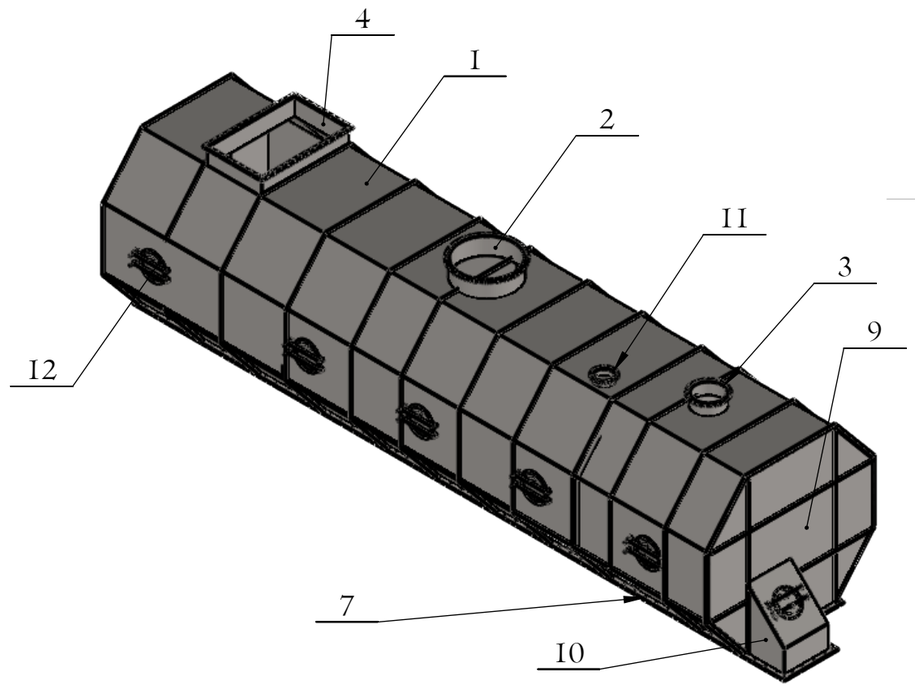

ITEM NO.	SHEET NUMBER	DESCRIPTION	Material	QTY.
12	34	DOOR	SEE SHEET	5
II	31	MANHOLE	SEE SHEET	I
10	20	OUTLET	SEE SHEET	I
9	19	PLATE	S.S304	I
8	18	PLATE	S.S304	I
7	17	FLANGE	ST52	I
6	12	VALVE	SEE SHEET	I
5	11	PLATE	S.S304	I
4	08	MNHOLE	SEE SHEET	I
3	05	MANHOLE	SEE SHEET	I
2	02	MANHOLE	SEE SHEET	I
I	SH1	BODY	S.S304	I

UNLESS OTHERWISE SPECIFIED,
DIMENSIONS ARE IN MILLIMETERS
GENERAL TOLERANCES:DIN 7168
LINEAR: m ANGULAR: S
FREE WELDING TOLERANCE:DIN 8570

FINISH:

DEBUR AND BREAK SHARP EDGES

FILE No:

DESCRIPTION:

FLUIDBED

MATERIAL:

WEIGHT:

SHEET 00

THIS DOCUMENT IS THE PROPERTY OF OWNER. IT IS CONFIDENTIAL AND ALL RIGHTS ARE RESERVED WITH REGARD TO IT. NO PART OF THIS MATERIAL MAY BE REPRODUCED IN ANY THIRD PARTY, REPRODUCED, STORED IN ANY RETRIEVAL SYSTEM OR TRANSMITTED IN ANY FORM OR BY ANY MEANS WITHOUT THE PRIOR WRITTEN CONSENT OF OWNER.

REV.	ISSUE DATE	DESCRIPTION	OWNER'S ACTION	DWG. BY	CHKD. BY	DEPT SUPR	PROJ. MGR
00	02/06/01	ISSUE FOR CONSTRUCTION	A	M.KAREVAN	R.DINZADEH	R.DINZADEH	M.ASGARIAN

OWNER: KAVEH GLASS INDUSTRY GROUP

PROJECT: SODIUM CARBONATE 2 SACHI

IFR ☐ Information ☐ Review ☐ Approve
IFC ☐ Review ☑ Approve
IFQ ☐
ASB ☐

PROJ.NO: 0003

TITLE: FLUIDBED

SCALE:

QTY.

DRAWING No: DWG-N52-RD-012

REV. 00